

## PLANTA PRIMER PISO

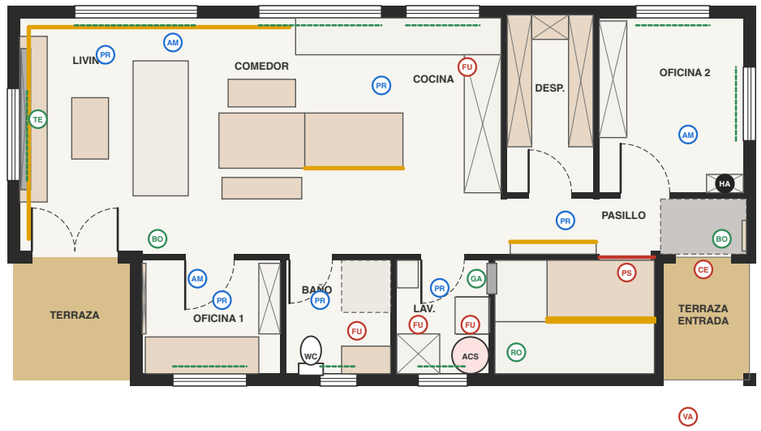


## PLANTA SEGUNDO PISO

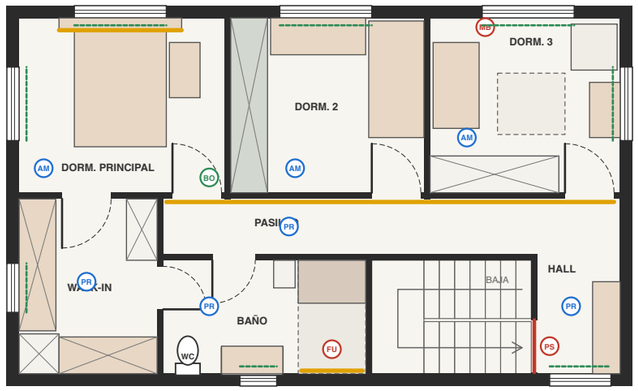


## SIMBOLOGÍA

- HA — Home Assistant + rack (en G2)
- PR — Sensor de presencia mmWave
- AM — Sensor ambiente T° / HR / $CO_2$ (zona piso radiante)
- FU — Sensor de fuga de agua
- VA — Válvula motorizada de corte de agua
- CE — Cerradura digital + videoportero
- PS — Contacto en puerta de seguridad
- MB — Monitor de bebé local (sin nube)
- TE — Motor del telón + proyector
- GA — Gatera con lector de microchip
- RO — Base de aspiradora robot
- BO — Botonera de escenas (reemplaza interruptor)
- LED indirecto regulable
- Cortina motorizada
- Puerta de seguridad

### ESCENAS (Home Assistant, funcionan sin internet)

| Escena | Se activa con | Qué hace |
|---|---|---|
| **Buenos días** | Alarma del celular, lun-vie | Cortinas suben, cabecero 30 % → 100 % en 15 min, ACS ok |
| **Cine** | Botonera living | Baja el telón, sube el proyector, cortinas cerradas, fosa LED 10 % |
| **Siesta bebé** | Botón en dorm. 3 | Timbre en silencio, pasillo P2 ámbar 5 %, VMC en modo bajo |
| **Llegada** | Cerradura abre con huella | Genkan + zapatero, clima a confort, aviso si puerta seguridad abierta |
| **Salir** | Botonera entrada | Apaga todo, baja temperatura 2 °C, cámaras y sensores de fuga en guardia |
| **Noche** | 23:00 o botón cabecero | Guía nocturna ámbar por presencia, puertas de seguridad vigiladas |
| **Sol a favor** | Excedente FV > 2 kW | Secadora, lavavajillas, ACS a 60 °C y carga del auto |
| **Fuga** | Cualquier sensor FU | Cierra la válvula general y avisa al celular |

### ARQUITECTURA DE LA DOMÓTICA

1. Controlador Home Assistant local en el armario técnico G2 (junto al TDA), con UPS. Sin nube obligatoria.
2. Protocolos abiertos: Zigbee 3.0 / Thread-Matter para sensores; Wi-Fi sólo para equipos grandes.
3. Se conservan los interruptores físicos: micromódulos Zigbee detrás (RIC 10, un efecto por luminaria).
4. Cat6 a cada recinto + PoE para cámaras y videoportero. Ducto vacío de reserva al entretecho.
5. Piso radiante: una zona por recinto, termostato = sensor AM; la bomba de calor recibe SG-Ready.
6. VMC sube automáticamente con $CO_2$ > 900 ppm o HR > 65 % (baños, cocina, lavandería).
7. Cortinas motorizadas a batería recargable (sin cordones: seguridad bebé y gatos).
8. Ver INTERIORISMO.md para equipos sugeridos, etapas y presupuesto.

### EQUIPOS POR ETAPA (referencial 2026, cotizar)

| Etapa | Equipos | CLP |
|---|---|---|
| 1 · Obra gruesa | Cat6 a cada recinto, ducto de reserva, cajas profundas tras interruptores, enchufe en G2 | 0,3–0,5 MM |
| 2 · Mudanza | Home Assistant (mini PC) + coordinador Zigbee/Thread, cerradura digital, 6 sensores de fuga + válvula | 0,6–0,9 MM |
| 3 · Confort | Sensores AM por zona, presencia mmWave, micromódulos en interruptores, contactos puertas seg. | 0,6–1,0 MM |
| 4 · Cuando haya capital | Cortinas motorizadas (17 ventanas), telón + proyector UST, LED indirecto, videoportero PoE | 2,5–4,5 MM |

Medidas aproximadas — verificar en terreno. +Y = norte geográfico.

| | |
|---|---|
| PROYECTO | VIVIENDA 2 PISOS — ANTEPROYECTO |
| LÁMINA | **ILUMINACIÓN Y DOMÓTICA** |
| ESCALA | 1:100 (imprimir en A3) |
| FECHA | 20-10-2026 |
| CÓDIGO | INT-02 · 11 de 11 |