

PLANTA PRIMER PISO

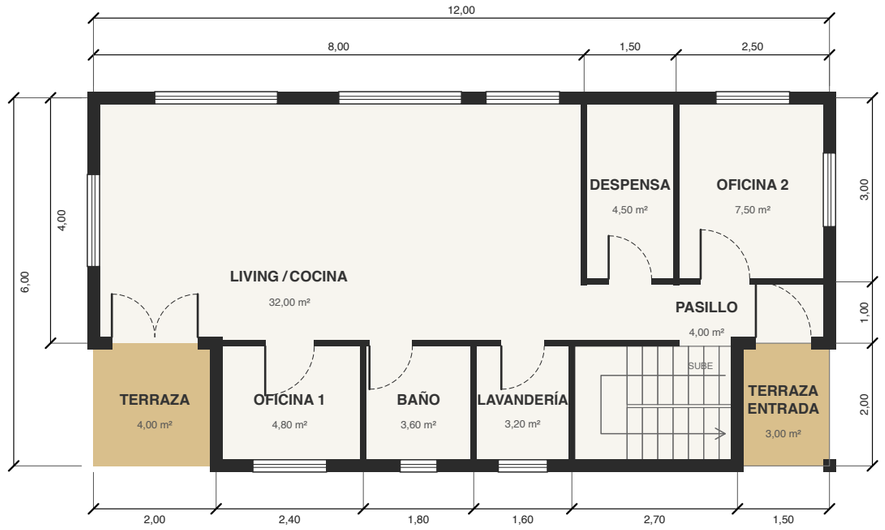

PLANTA SEGUNDO PISO

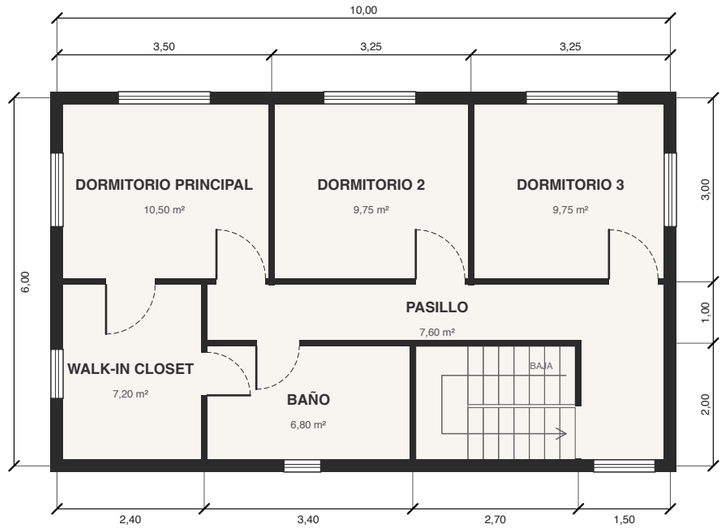

SIMBOLOGÍA


- Muro / tabique
- Ventana
- Puerta (abatimiento)
- Terraza exterior

CUADRO DE SUPERFICIES	m²
Primer piso	65,00
Segundo piso	60,00
Total edificado	125,00
Terrazas (no edificadas)	7,00
Superficies medidas a eje de muros	

NOTAS

1. Medidas en metros, a eje de muro. Escala 1:100 en A3.
2. Muros exteriores 20 cm, tabiques 10 cm. Altura piso-cielo 2,50 m.
3. Entrepiso: losa 20 cm. Nivel piso 2 = +2,70 m.
4. Escalera en U: 15 contrahuellas de 18 cm, huellas 25 cm, tramos de 0,90 m. Cabe justo en la franja de 2 m de fondo. Llega al piso 2 por el hall sobre la terraza de entrada.
5. Medidas inferidas del boceto: ajustar en casa_datos.py y regenerar con python3 generar_laminas.py

VISTA 3D desde el NE (modelo FreeCAD)

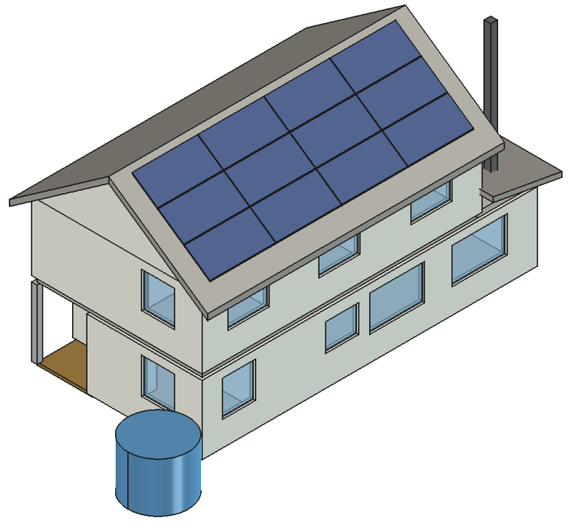

Medidas aproximadas — verificar en terreno. +Y = norte geográfico.

PROYECTO	VIVIENDA 2 PISOS — ANTEPROYECTO
LÁMINA	**PLANTAS DE ARQUITECTURA**
ESCALA	1:100 (imprimir en A3)
FECHA	20-10-2026
CÓDIGO	ARQ-01 · 1 de 9