
PLANTA DE OBRAS EXTERIORES

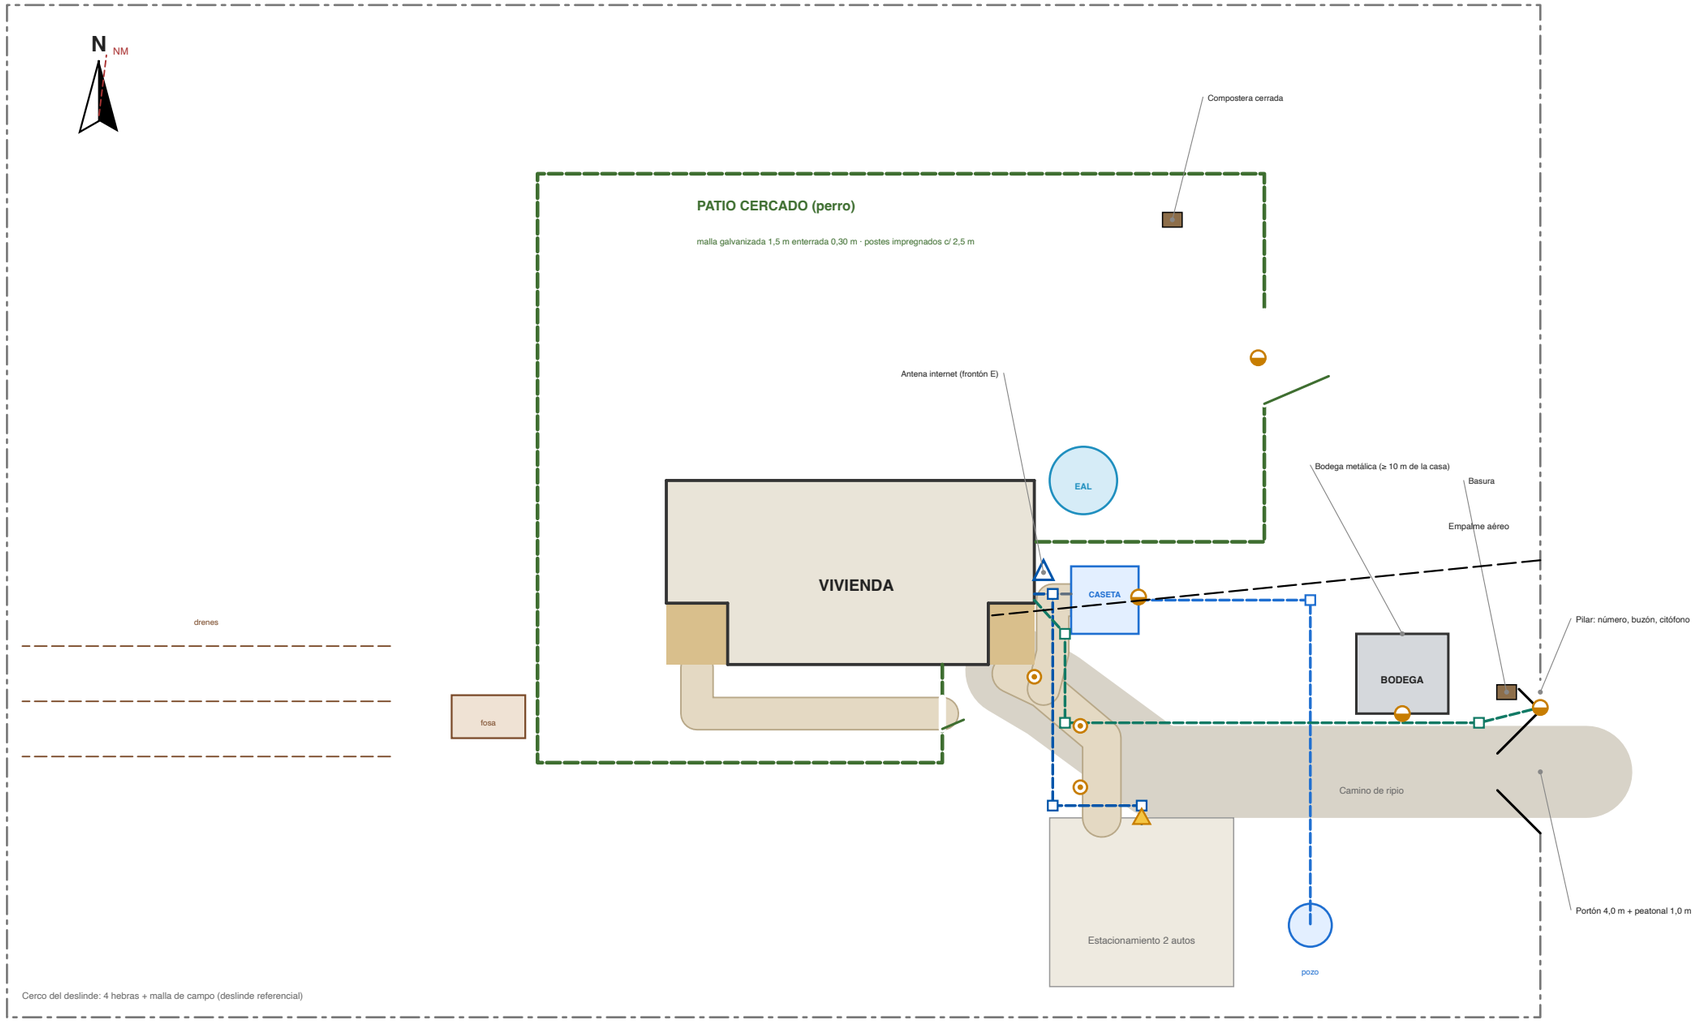

SIMBOLOGÍA

- Cerco patio (perro)
- Cerco del deslinde
- Sendero pavimentado
- Baliza de sendero
- Foco con sensor
- Aplique exterior
- Ducto C15 + datos
- Ducto cargador EV
- Ducto C8 caseta
- Cable bomba del pozo
- Cámara de paso 40×40
- Residuos

CRITERIOS

1. El patio usa la casa como parte del cierre: la entrada, la caseta, la fosa y el estacionamiento quedan fuera (camión limpiafosas sin abrir el patio).
2. La malla enterrada evita que el perro excave. Los gatos no se contienen con cerco.
3. Bodega metálica a ≥ 10 m de la casa (CONAF): no hay leña ni combustibles junto a los muros.
4. Luz cálida 2700 K hacia abajo (fauna, cielo oscuro); se enciende con sensor y escena HA.
5. Zanja común a 0,60 m: energía y datos en ductos separados ≥ 0,20 m, cinta de advertencia encima.
6. Senderos drenantes: el barro de Los Ríos queda fuera del genkan.
7. Basura cerrada junto al camino (recolección rural), compost dentro del patio en compostera cerrada.
8. Fajas CONAF, fosa, drenes y aguas lluvias: EMP-01.

CUADRO DE OBRAS EXTERIORES (cantidades del dibujo; cotizar con el deslinde real)

Ítem	Especificación	Cantidad
Patio cercado (perro)	Malla galv. 1,5 m enterrada 0,30 m, postes 3×3" impregnados c/ 2,5 m	78,80 m
Puertas del patio	Peatonal 1,0 m con cierre automático + portón 3,0 m de jardín	2 u
Cerco del deslinde	4 hebras + malla de campo (largo referencial: definir con la escritura)	161 m
Portón de acceso	Vehicular 4,0 m batiente con motor 24 V y batería + peatonal 1,0 m	1 + 1 u
Pilar de acceso	Número iluminado, buzón, citófono IP, caseta de basura cerrada	1 u
Senderos	Adoquín o baldosa sobre base compactada 15 cm, drenante	20,53 m²
Bodega exterior	Metálica 3,0 × 2,6 m sobre radier, luz y enchufe (C15)	7,80 m²
Luminarias exteriores	LED 2700 K apantalladas, sensor + crepuscular (C15)	3 bal. · 1 foco · 4 apl.
Ductos enterrados	Zanja 0,60 m, energía y datos separados, cinta, cámaras 40×40	48 m
Residuos	Caseta de basura junto al camino + compostera de 2 cámaras	2 u
Internet rural	Antena 4G/5G o satelital en frontón E + ducto al rack	1 u

Medidas aproximadas — verificar en terreno. +Y = norte geográfico.

PROYECTO	VIVIENDA 2 PISOS — ANTEPROYECTO
LÁMINA	**OBRAS EXTERIORES: CERCO, ACCESOS, LUCES Y DUCTOS**
ESCALA	1:200
FECHA	20-10-2026
CÓDIGO	EXT-01 · 13 de 14