

PLANTA PRIMER PISO

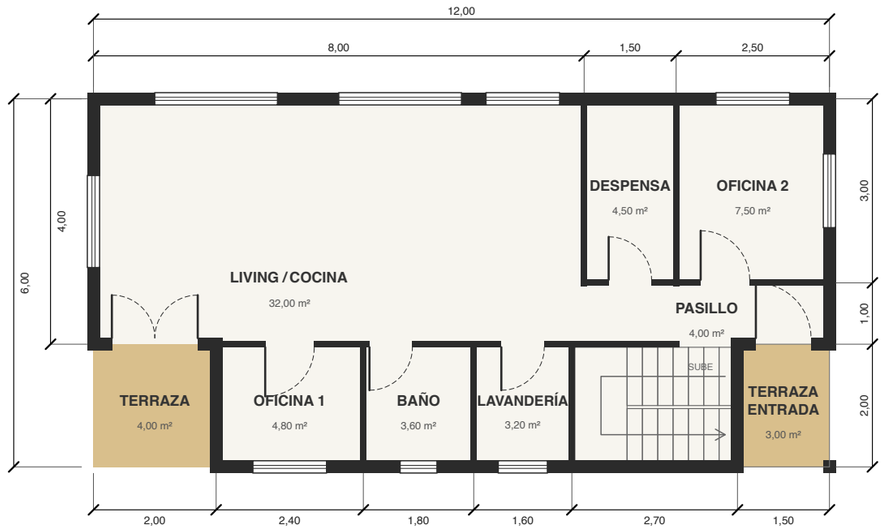

PLANTA SEGUNDO PISO

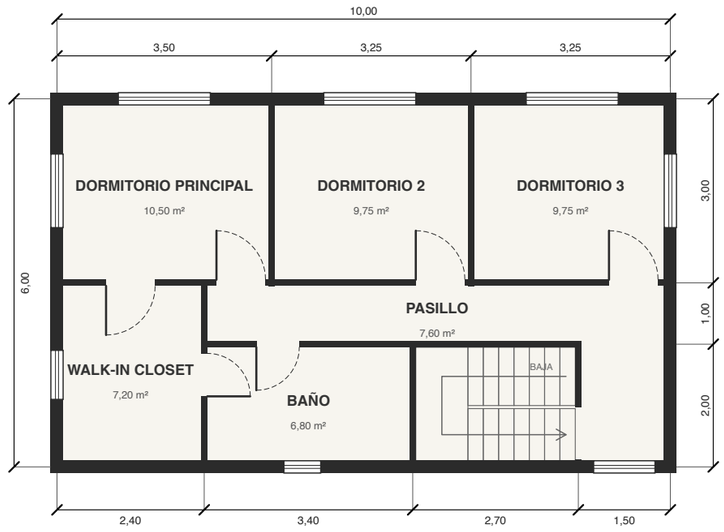

SIMBOLOGÍA


- Muro / tabique
- Ventana
- Puerta (abatimiento)
- Terraza exterior

CUADRO DE SUPERFICIES	m²
Primer piso	65,00
Segundo piso	60,00
Total edificado	125,00
Terrazas (no edificadas)	7,00
Superficies medidas a eje de muros	

NOTAS

1. Medidas en metros, a eje de muro. Escala 1:100 en A3.
2. Muros exteriores 20 cm, tabiques 10 cm. Piso-cielo P1 2,36 m, P2 2,50 m (≥ 2,30, OGUC 4.1.1).
3. Entrepiso acústico de madera 34 cm (piso flotante + cielo desacoplado, detalle en ELE-02). Nivel piso 2 = +2,70 m. El P2 no lleva piso radiante.
4. Escalera en U: 15 contrahuellas de 18 cm, huellas 25 cm, tramos de 0,90 m. Cabe justo en la franja de 2 m de fondo. Llega al piso 2 por el hall sobre la terraza de entrada. Baranda 0,95 m (0,85 en tramo), sin huecos > 12,5 cm, y puertas de seguridad arriba y abajo (bebé, gatos).
6. Ventanas P2 con antepecho 1,00 m y limitador de apertura 10 cm.
7. Superficie ≤ 140 m² y 2 pisos → F-15 (OGUC 4.3.5 n°14), DS1 ok.
8. Mesones 0,85 m y muebles altos a 1,40 m (estatura 1,64 m).
9. Medidas en casa_datos.py; regenerar: python3 generar_laminas.py

VISTA 3D (modelo FreeCAD)

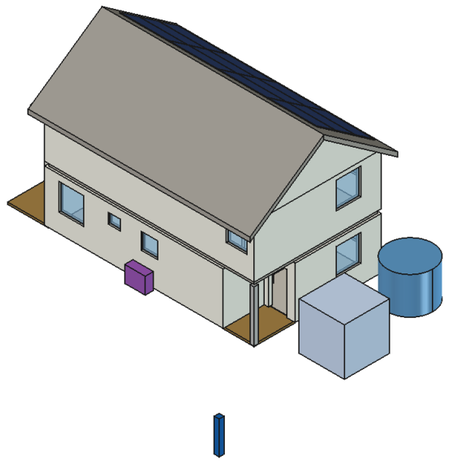

Medidas aproximadas — verificar en terreno. +Y = norte geográfico.

PROYECTO	VIVIENDA 2 PISOS — ANTEPROYECTO
LÁMINA	**PLANTAS DE ARQUITECTURA**
ESCALA	1:100 (imprimir en A3)
FECHA	20-10-2026
CÓDIGO	ARQ-01 · 1 de 13